



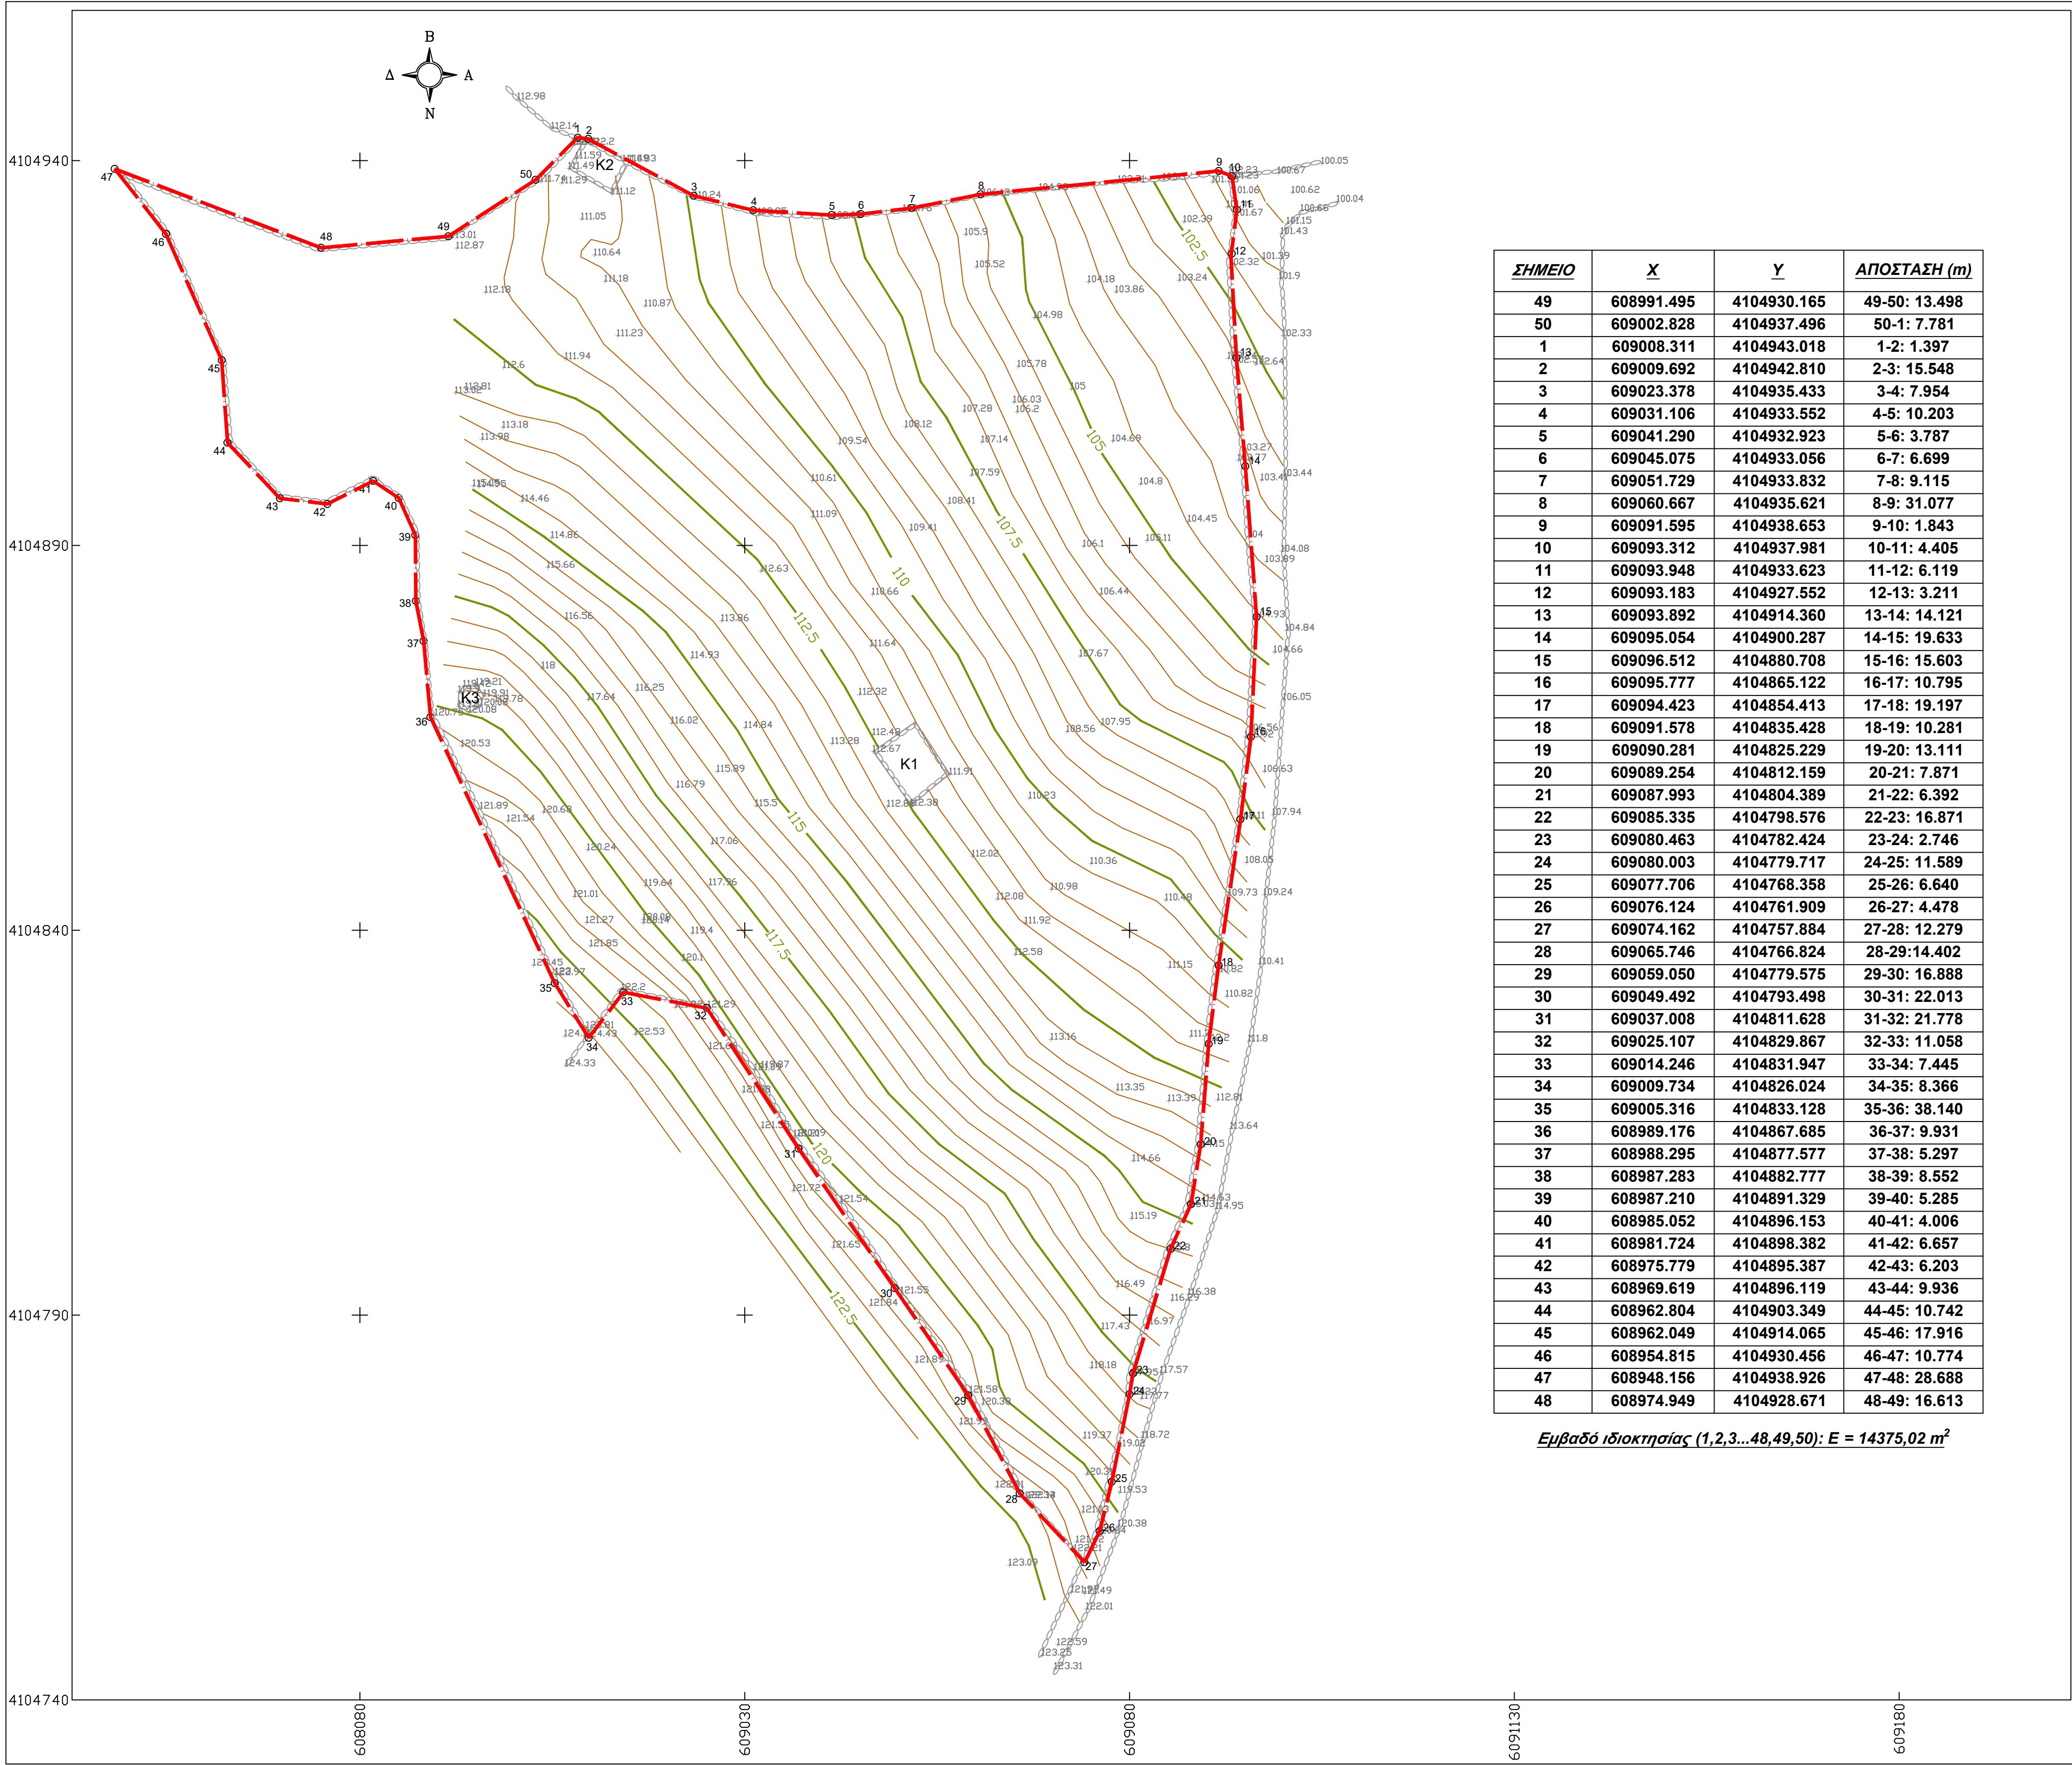


ΣΗΜΕΙΟ	X	Y	ΑΠΟΣΤΑΣΗ (m)
49	608991.495	4104930.165	49-50: 13.498
50	609002.828	4104937.496	50-1: 7.781
1	609008.311	4104943.018	1-2: 1.397
2	609009.692	4104942.810	2-3: 15.548
3	609023.378	4104935.433	3-4: 7.954
4	609031.106	4104933.552	4-5: 10.203
5	609041.290	4104932.923	5-6: 3.787
6	609045.075	4104933.056	6-7: 6.699
7	609051.729	4104933.832	7-8: 9.115
8	609060.667	4104935.621	8-9: 31.077
9	609091.595	4104938.653	9-10: 1.843
10	609093.312	4104937.961	10-11: 4.405
11	609093.948	4104933.623	11-12: 6.119
12	609093.183	4104927.552	12-13: 3.211
13	609093.892	4104914.360	13-14: 14.121
14	609095.054	4104900.287	14-15: 19.633
15	609096.512	4104880.708	15-16: 15.603
16	609095.777	4104865.122	16-17: 10.795
17	609094.423	4104854.413	17-18: 19.197
18	609091.578	4104835.428	18-19: 10.281
19	609090.281	4104825.229	19-20: 13.111
20	609089.254	4104812.159	20-21: 7.871
21	609087.993	4104804.389	21-22: 6.392
22	609085.335	4104798.576	22-23: 16.871
23	609080.463	4104782.424	23-24: 2.746
24	609080.003	4104779.717	24-25: 11.589
25	609077.706	4104768.358	25-26: 6.640
26	609076.124	4104761.909	26-27: 4.478
27	609074.162	4104757.884	27-28: 12.279
28	609065.746	4104766.824	28-29: 14.402
29	609059.050	4104779.575	29-30: 16.888
30	609049.492	4104793.498	30-31: 22.013
31	609037.008	4104811.628	31-32: 21.778
32	609025.107	4104829.867	32-33: 11.058
33	609014.246	4104831.947	33-34: 7.445
34	609009.734	4104826.024	34-35: 8.366
35	609005.316	4104833.128	35-36: 38.140
36	608989.176	4104867.685	36-37: 9.931
37	608988.295	4104877.577	37-38: 5.297
38	608987.283	4104882.777	38-39: 8.552
39	608987.210	4104891.329	39-40: 5.285
40	608985.052	4104896.153	40-41: 4.006
41	608981.724	4104898.382	41-42: 6.657
42	608975.779	4104895.387	42-43: 6.203
43	608969.619	4104896.119	43-44: 9.936
44	608962.804	4104903.349	44-45: 10.742
45	608962.049	4104914.065	45-46: 17.916
46	608954.815	4104930.456	46-47: 10.774
47	608948.156	4104938.926	47-48: 28.688
48	608974.949	4104928.671	48-49: 16.613

Εμβαδό ιδιοκτησίας (1,2,3...48,49,50): Ε = 14375,02 μ²

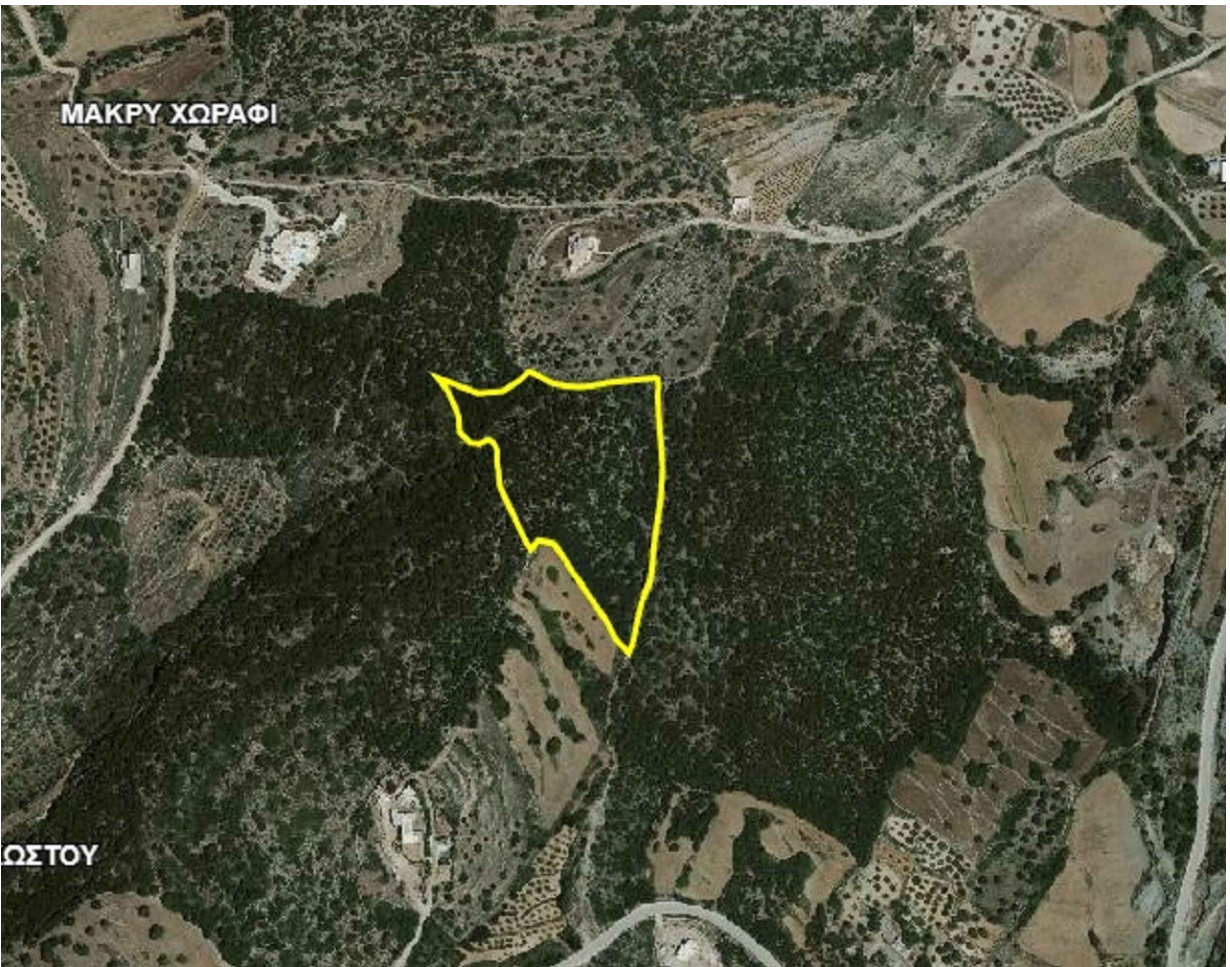

ΕΝΤΟΠΙΣΜΟΣ ΓΗΠΕΔΟΥ ΕΠΙ ΟΡΘΟΓΩΝΙΟΧΑΡΤΗ ΚΛΙΜΑΚΑΣ 1:5000

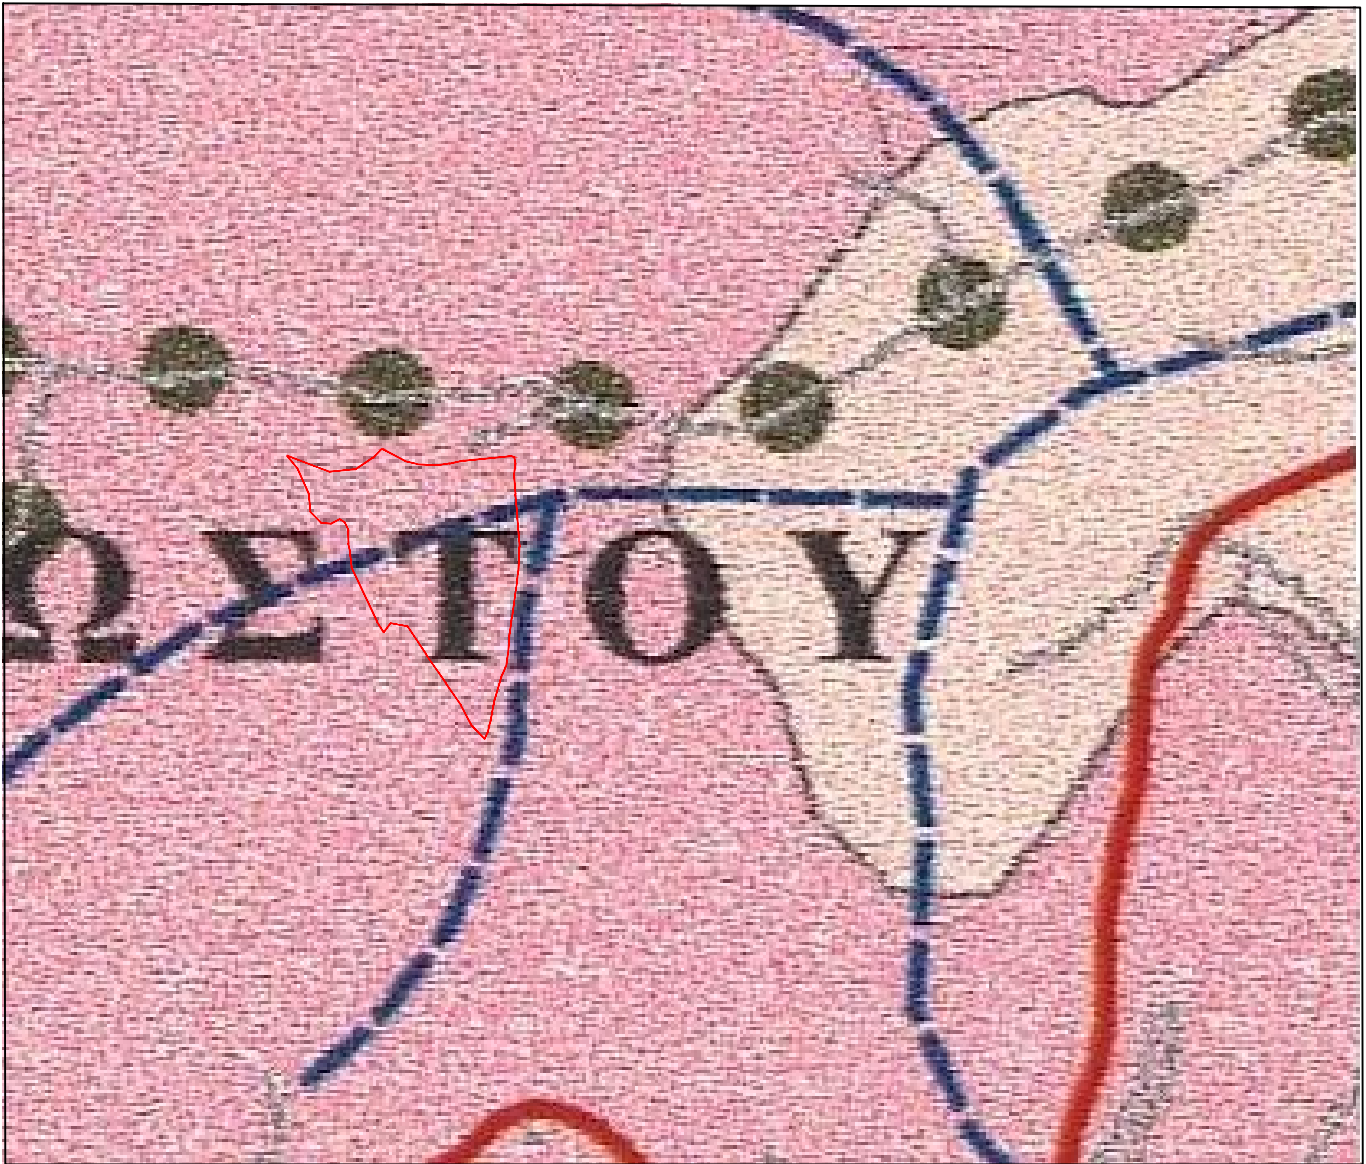

ΥΠΟΜΝΗΜΑ		
ΥΦΙΣΤΑΜΕΝΕΣ ΚΑΤΑΣΤΑΣΕΙΣ		
Δ/Α	ΠΕΡΙΓΡΑΦΗ	ΕΜΒΑΔΟ (m2)
K1	Κτίσμα λθόκτιστο ερειπωμένο προ του 1955	55
K2	Κτίσμα λθόκτιστο ερειπωμένο προ του 1955	30
K3	Πηγάδι - λθόκτιστη δεξαμενή	10

— 2.50 — ΚΥΡΙΑ ΙΣΟΥΝΗΣ ΚΑΜΠΥΛΗ
— — ΔΕΥΤΕΡΕΥΟΥΣΑ ΙΣΟΥΝΗΣ ΚΑΜΠΥΛΗ
— — ΤΟΠΟΣ ΑΠΟ ΞΗΡΟΝΙΣΙΑ
— — ΟΡΙΟ ΙΔΙΟΚΤΗΤΕΙΑΣ

ΟΡΟΙ ΔΟΜΗΣΗΣ - ΧΡΗΣΕΙΣ ΓΗΣ

Το παρόν αγροτεμάχιο υπάγεται στην Περιμετρική Ζώνη Ενδοχώρας Π.Ε.Π.Δ. 2, σύμφωνα με το ΦΕΚ 148/ΑΑΠ 2-5-2012 (Γ.Π.Σ. Παρού Άρθρο 3, Παρ. 3.4.2) και ισχύουν:

Αρδίαση:

Όσο κατισχύει - αρδίασης: 8 στρ.

Παρέκλιση: Προ 7-7-1993 4 στρ.

Δεν ισχύει άλλη παρέκλιση.

Αρδίαση τουριστικών εγκαταστάσεων: 15 στρ.

Όροι και περιορισμοί δόμησης:

- το Π.Δ. 16-06-1993, ΦΕΚ 732Δ/07-07-1993 «Καθορισμός χρήσεων γης και όρων και περιορισμών των εκτός σχεδίου και εκτός ορίων οικισμών περιοχών των νήσων Παρού και Αντιπάρου Ν. Κυκλάδων»
- το Π.Δ. 24/31-05-1985 «Εκτός Σχεδίου δόμηση» ΦΕΚ 270Δ/1985, όπως τροποποιήθηκε με το Ν.3212/2003 (ΦΕΚ 308/Α) και το Ν.4759/2020 (ΦΕΚ 245Α/2020).

ΣΗΜΕΙΩΣΕΙΣ

- ΜΕΘΩΔΟΣ: ΕΠΙΓΕΙΑ ΑΠΟΤΥΠΩΣΗ.
- Ο ΥΠΟΛΟΓΙΣΜΟΣ ΤΟΥ ΕΜΒΑΔΟΥ Ε(1,2,3...48,49,50) = 14375,02 μ² ΕΓΙΝΕ ΣΥΜΦΩΝΑ ΜΕ ΤΙΣ ΑΠΟΛΥΤΕΣ ΣΥΝΤΕΤΑΓΜΕΝΕΣ ΤΩΝ ΚΟΡΥΦΩΝ ΤΟΥ ΓΗΠΕΔΟΥ, ΜΕ ΤΟΝ ΙΔΙΟ ΤΡΟΠΟ ΥΠΟΛΟΓΙΣΤΗΚΑΝ ΚΑΙ ΤΑ ΜΗΚΗ ΤΩΝ ΠΛΕΥΡΩΝ ΤΟΥ.
- ΤΟ ΣΥΣΤΗΜΑ ΣΥΝΤΕΤΑΓΜΕΝΩΝ ΕΙΝΑΙ ΤΟ ΚΡΑΤΙΚΟ ΕΓΣΑ 1987, Η ΕΞΑΡΤΗΤΗ ΕΓΙΝΕ ΣΥΜΦΩΝΑ ΜΕ ΤΗ ΜΕΘΩΔΟ RTK ΤΟΥ ΝΕΡΟΣ.
- ΤΑ ΟΡΙΑ, ΟΠΩΣ ΕΜΦΑΝΙΟΝΤΑΙ ΣΤΟ ΠΑΡΟΝ ΔΙΑΓΡΑΜΜΑ, ΥΠΕΔΕΙΧΘΗΣΑΝ ΑΠΟ ΤΩΝ ΙΔΙΟΚΤΗΤΗ.
- ΙΣΟΔΙΑΣΤΑΣΗ ΥΦΟΜΕΤΡΙΚΩΝ ΚΑΜΠΥΛΩΝ 0,5 m.
- ΥΦΟΜΕΤΡΙΚΗ ΑΦΕΤΗΡΙΑ ΑΠΟΤΕΛΕΙ Η ΜΕΧΗ ΣΤΑΘΜΗ ΘΑΛΑΣΣΑΣ.

ΔΗΛΩΣΗ ΜΗΧΑΝΙΚΟΥ (Ν. 651/77)

Δηλώνω σύμφωνα με το νόμο, για το αγροτεμάχιο με στοιχεία «1,2,3...48,49,50» και εμβαδόν 14375,02 μ², που βρίσκεται στη θέση «Κακιάδι» της Δ.Κ. Κώστου της Δ.Ε. Παρού του Δήμου Παρού της Π.Ε. Παρού, ότι:

α) Βρίσκεται **εκτός σχεδίου και εκτός ορίων οικισμού**.

β) Είναι **άγρια** ως προς το εμβαδόν και τις διαστάσεις, σύμφωνα με τις ισχύουσες πολεοδομικές διατάξεις, ΦΕΚ 148/ΑΑΠ 2-5-2012, Π.Δ. 16-6-1993 ΦΕΚ 732Δ/1993 και Π.Δ. 24/31-05-1985 ΦΕΚ 270Δ/1985 (όπως τροποποιήθηκε και ισχύει).

γ) Είναι **μη οικοδομήσιμα**, ως ανήκον σε δοσική περιοχή σύμφωνα με τους κυρωμένους δοσικούς χάρτες της ν. Παρού

δ) Σύμφωνα με το Γενικό Πολεοδομικό Σχέδιο του Δήμου Παρού, ΦΕΚ 148/ΑΑΠ 2-5-2012, το αγροτεμάχιο βρίσκεται στην Περιμετρική Ζώνη Ενδοχώρας Π.Ε.Π.Δ. 2.

ε) **Δεν εμπόδισ**ε στις διατάξεις του Ν. 1337/83 περί εισαγωγών σε γη και χρήμα.

ζ) Εντός αυτού δε διέρχονται ενσέρως γραμμές μεταφοράς υψηλής τάσης της ΔΕΗ ή αγωγός φυσικού αερίου.

η) Απύχει από παραδοσιακή οικισμό απόσταση μεγαλύτερη των 500,00 m.

θ) Τα εντός του αγροτεμαχίου κτίσματα K1 και K2 προϋφίστανται προ 1955 και χρήζουν ανασκαφικών.

Η ΜΗΧΑΝΙΚΟΣ

ΚΥΡΙΑΚΗ Γ. ΠΑΝΤΕΛΑΙΟΥ
ΔΙΠΛ. ΑΓΡΟΝΟΜΟΣ - ΤΟΠΟΓΡΑΦΟΣ ΜΗΧΑΝΙΚΟΣ
ΠΟΛΙΤΕΚΝΙΟΝ ΔΥΤΙΚΗΣ Α. Π. ΘΕΣΣΟΝΙΚΗΣ
ΜΕΛΟΣ ΤΗΣ ΕΠΕΛΕΓΜΕΝΗΣ ΜΗΤΡΟΥΣ 33339
ΝΑΞΟΥ 11 ΧΑΛΛΑΔΡΙ 15238 - ΤΗΛ 5353458
ΑΦΜ. 924363367 - ΔΟΥ ΧΑΛΛΑΔΡΙΟΥ

ΔΗΛΩΣΗ ΙΔΙΟΚΤΗΤΗ

Ο ΚΑΤΩΘΙ ΥΠΟΓΡΑΦΜΕΝΟΣ ΒΑΡΩΤΣΗΣ ΜΑΡΙΟΣ, ΔΗΛΩΝΩ ΟΤΙ:

- ΤΑ ΟΡΙΑ ΤΗΣ ΙΔΙΟΚΤΗΤΕΙΑΣ ΜΟΥ ΜΕ ΣΤΟΙΧΕΙΑ 1,2,3...48,49,50, ΕΜΒΑΔΟΥ 14375,02 μ² ΠΟΥ ΚΕΙΤΑΙ ΣΤΗ ΘΕΣΗ «ΚΑΚΙΑΔΙ» Δ.Κ. ΚΩΣΤΟΥ Δ.Ε. ΠΑΡΟΥ Δ. ΠΑΡΟΥ Π.Ε. ΠΑΡΟΥ, ΥΠΕΔΕΙΧΘΗΣΑΝ ΑΠΟ ΕΜΕΝΑ.
- ΕΥΘΥΝΟΜΑΙ ΠΑ ΤΗΝ ΑΚΡΙΒΕΙΑ ΤΩΝ ΔΗΛΟΥΜΕΝΩΝ ΟΡΙΩΝ ΤΟΥ ΓΗΠΕΔΟΥ.

Ο ΔΗΛΩΝ

ΚΥΡΙΑΚΗ ΠΑΝΤΕΛΑΙΟΥ
ΑΓΡΟΝΟΜΟΣ - ΤΟΠΟΓΡΑΦΟΣ ΜΗΧΑΝΙΚΟΣ

ΝΑΣΟΥ 14
152 38 Κ. ΧΑΛΛΑΔΡΙ
ΤΗΛ. 2106080566, 6944617761
e-mail: kyran@tee.gr

ΒΑΡΩΤΣΗΣ ΜΑΡΙΟΣ

ΠΕΡΙΟΧΗ ΘΕΣΗ «ΚΑΚΙΑΔΙ» Δ.Κ. ΚΩΣΤΟΥ Δ.Ε. ΠΑΡΟΥ Δ. ΠΑΡΟΥ Π.Ε. ΠΑΡΟΥ ΠΕΡ. ΝΟΤΙΟΥ ΑΙΓΑΙΟΥ

ΑΡ. ΣΧΕΔΙΟΥ:

T-1

ΚΛΙΜΑΚΑ

1:500

ΤΟΠΟΓΡΑΦΙΚΟ ΔΙΑΓΡΑΜΜΑ

ΧΡΟΝΟΣ ΜΕΛΕΤΗΣ: ΦΕΒΡΟΥΑΡΙΟΣ 2024

ΥΠΟΓΡΑΦΗ

ΣΦΡΑΓΙΔΑ

ΚΥΡΙΑΚΗ Γ. ΠΑΝΤΕΛΑΙΟΥ
ΔΙΠΛ. ΑΓΡΟΝΟΜΟΣ - ΤΟΠΟΓΡΑΦΟΣ ΜΗΧΑΝΙΚΟΣ
ΠΟΛΙΤΕΚΝΙΟΝ ΔΥΤΙΚΗΣ Α. Π. ΘΕΣΣΟΝΙΚΗΣ
ΜΕΛΟΣ ΤΗΣ ΕΠΕΛΕΓΜΕΝΗΣ ΜΗΤΡΟΥΣ 33339
ΝΑΞΟΥ 11 ΧΑΛΛΑΔΡΙ 15238 - ΤΗΛ 5353458
ΑΦΜ. 924363367 - ΔΟΥ ΧΑΛΛΑΔΡΙΟΥ