


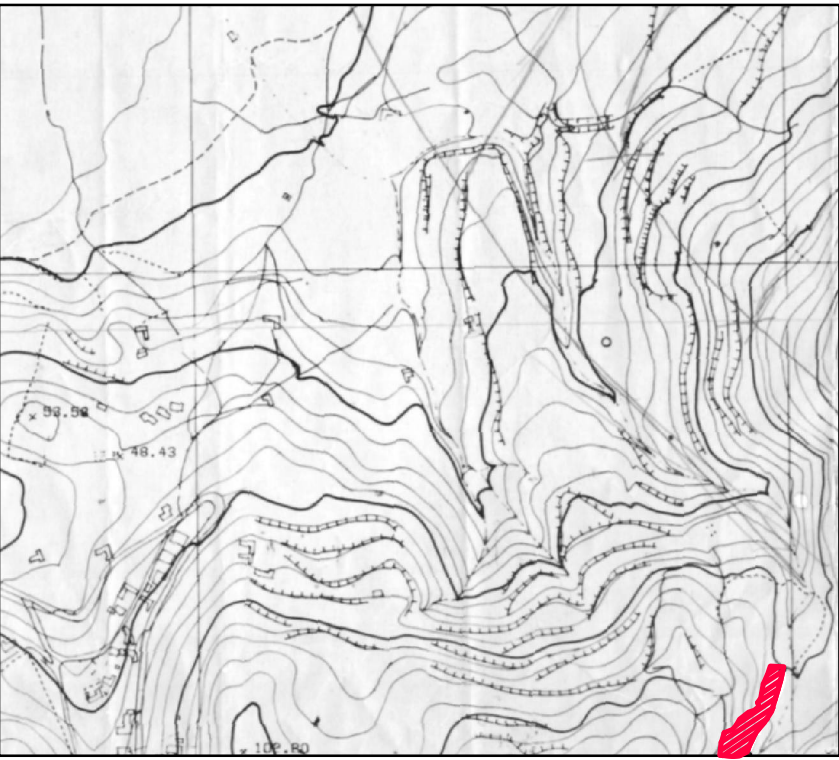

ΑΠΟΣΠΑΣΜΑ ΧΑΡΤΗ ΓΥΣ 7641_2



ΑΠΟΣΠΑΣΜΑ ΟΡΘΟΦΩΤΟΧΑΡΤΗ ΑΠΟ ΕΚΧΑ ΑΕ


ΣΥΣΤΗΜΑ ΣΥΝΤΕΤΑΓΜΕΝΩΝ ΕΓΣΑ '87

Εμβαδόν Γηπέδου				
Υπολογισμός Εμβαδού με Ορθογώνιες Συντεταγμένες				
	Α/Α	Σημείο	X	Y
1	1	1	625781.59	4103954.72
2	2	2	625782.76	4103964.69
3	3	3	625784.46	4103970.11
4	4	4	625785.30	4103973.44
5	5	5	625792.34	4103976.24
6	6	6	625795.56	4103980.29
7	7	7	625798.39	4103984.97
8	8	8	625806.04	4103990.46
9	9	9	625810.69	4103992.21
10	10	10	625813.69	4103994.86
11	11	11	625814.19	4103996.27
12	12	12	625813.55	4103998.51
13	13	13	625816.13	4104002.34
14	14	14	625818.37	4104014.46
15	15	15	625821.86	4104022.98
16	16	16	625823.76	4104029.41
17	17	17	625835.15	4104028.43
18	18	18	625832.45	4104017.11
19	19	19	625828.68	4104003.93
20	20	20	625825.13	4103991.21
21	21	21	625819.18	4103982.14
22	22	22	625812.16	4103974.11
23	23	23	625806.26	4103962.63
24	24	24	625804.94	4103957.46
25	25	25	625798.38	4103954.64
26	26	26	625793.17	4103953.69
27	1	1	625781.59	4103954.72

ΕΜΒΑΔΟΝ Ε = 1324.77m²



Φωτογραφία

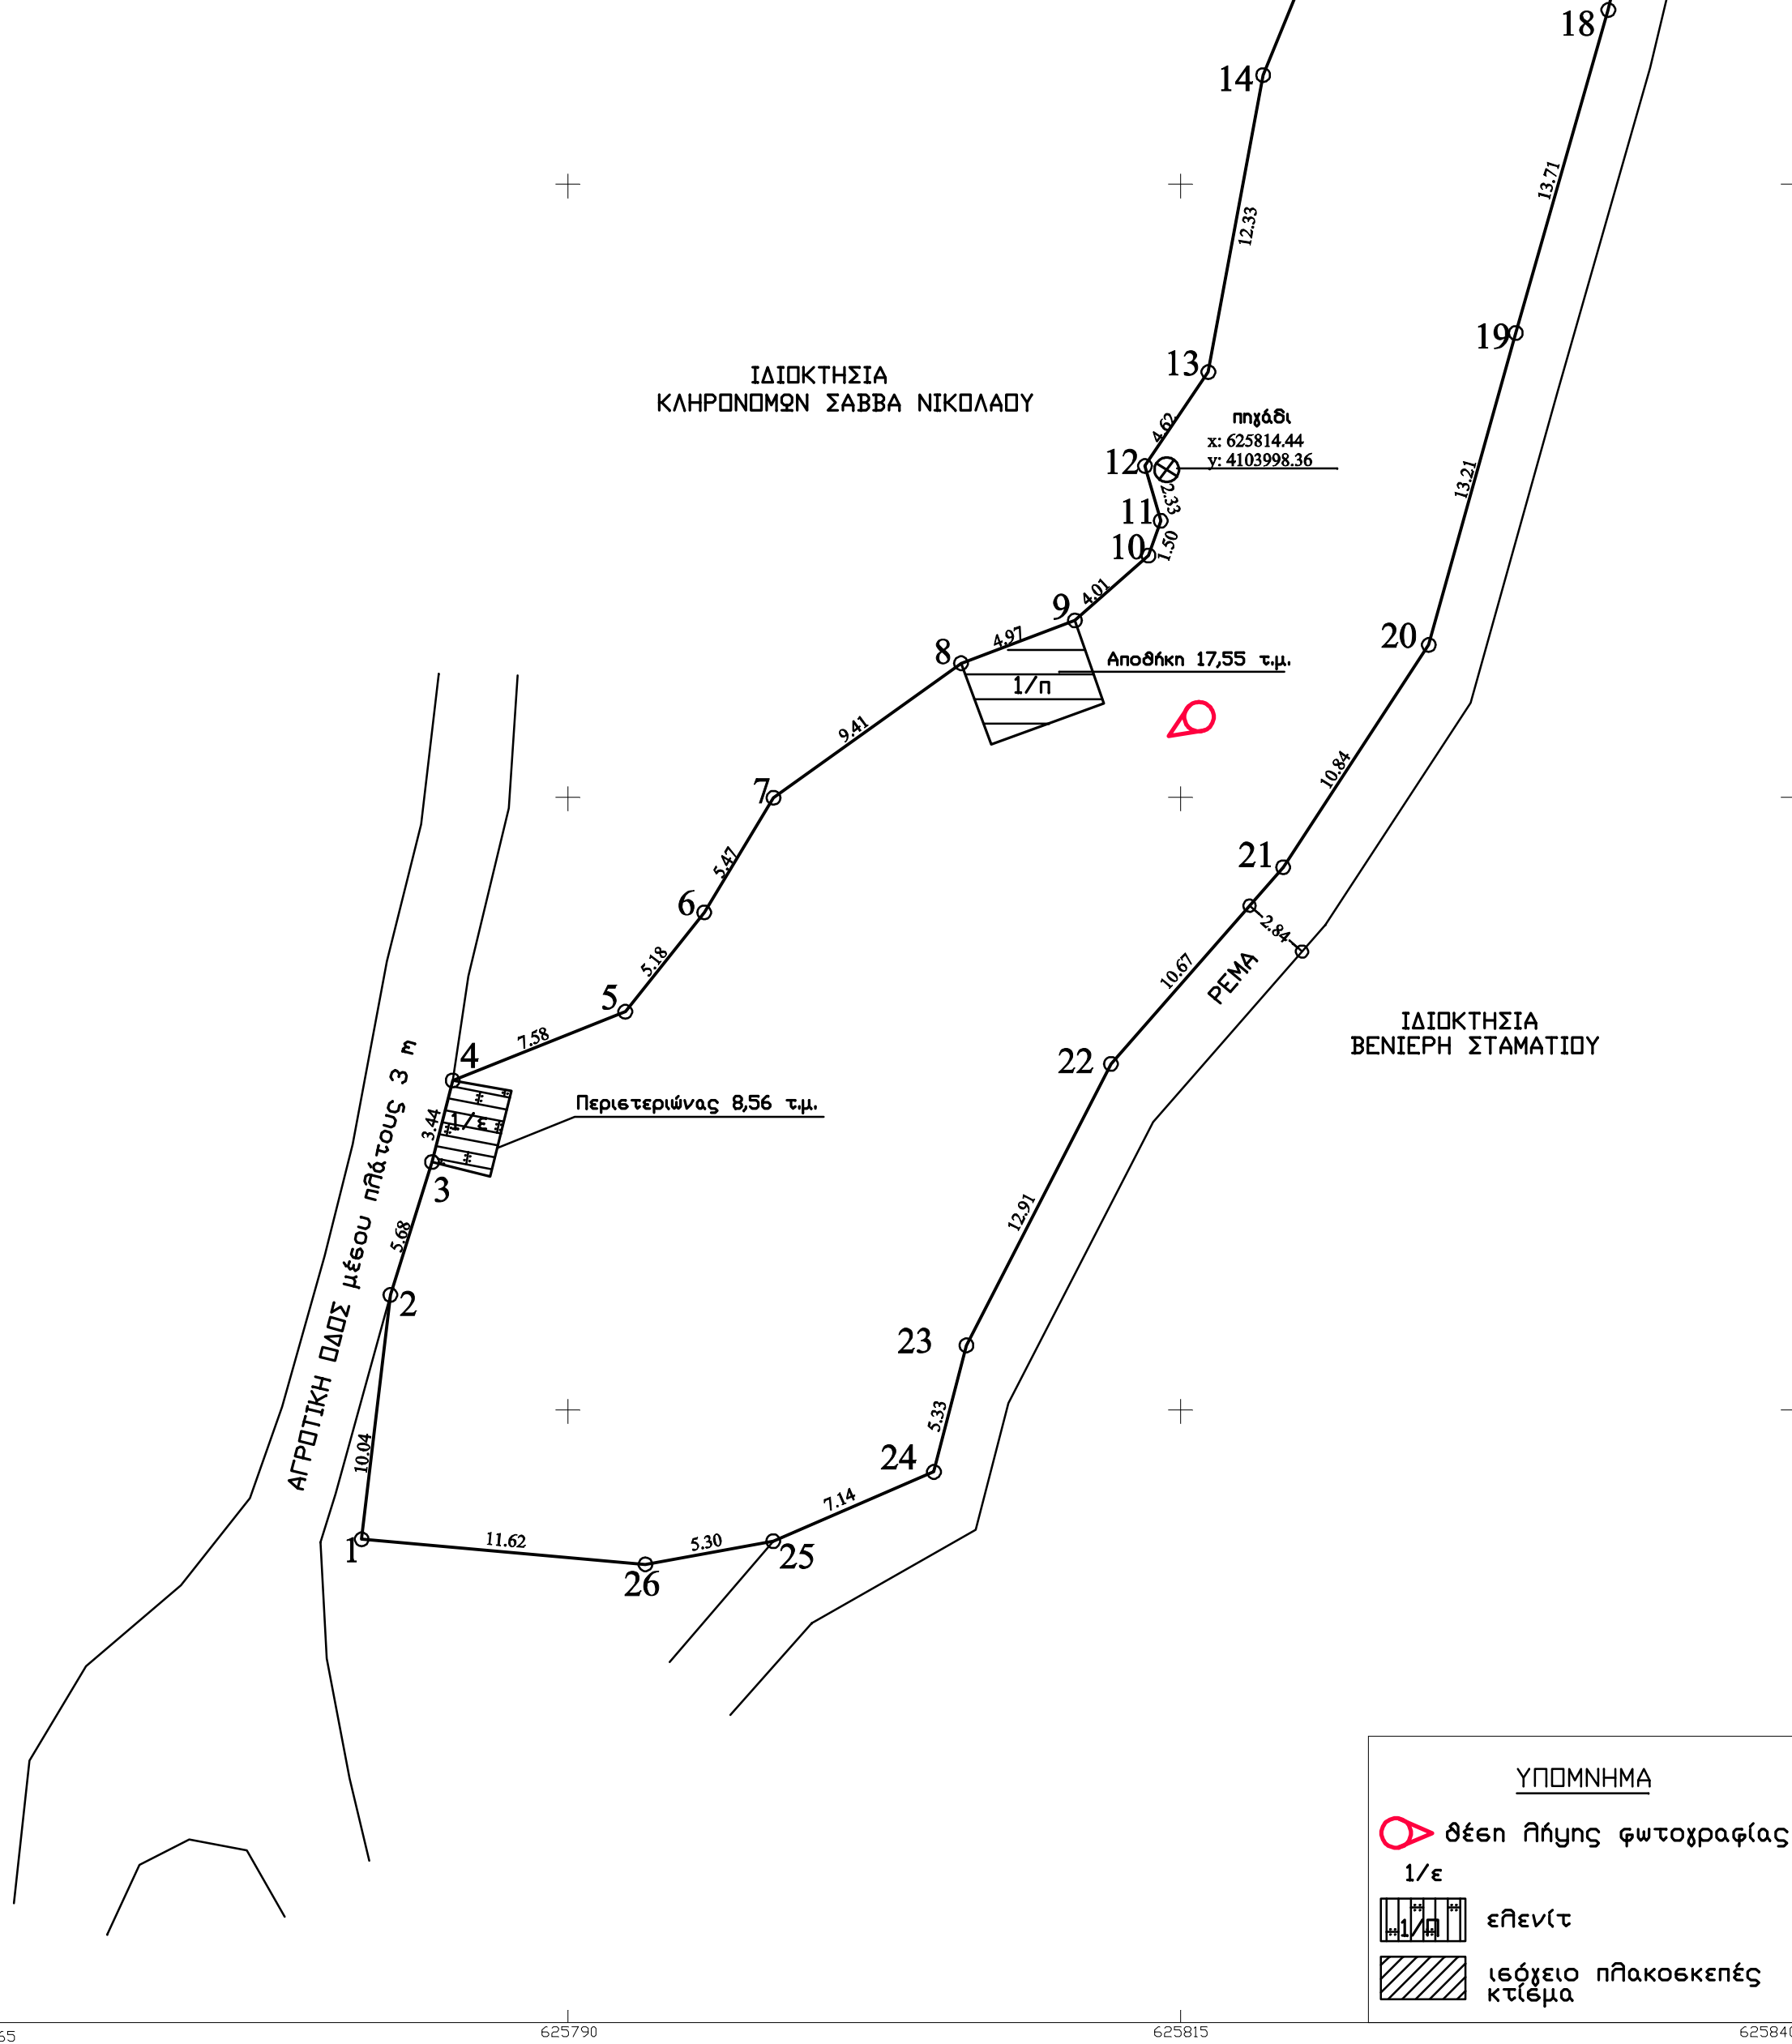

ΥΠΟΜΝΗΜΑ

θέση λήψης φωτογραφίας

1/ε

εξεν/τ

ισόγειο ηλιασκεπές κτίσμα

ΠΡΟΙ ΔΟΜΗΣΗΣ

ΕΚΤΟΣ ΟΡΙΩΝ ΟΙΚΙΣΜΟΥ (Π.Δ. 24.05.1985 – ΦΕΚ 270Δ / 31.05.1985 & Ν. 3212 – ΦΕΚ 308Α /31.12.2003 & Ν.3937 – ΦΕΚ 60Α / 31.3.2011)

Αρτιότητα κατά κανόνα: • για πρόσωπο σε κοινόχρηστο δρόμο)
Εμβαδόν = 4.000 τ.μ. – Πρόσωπο = 25.00 μ
• (για πρόσωπα σε Διεθνείς, Εθνικές, Επαρχιακές, Δημοτικές και Κοινοτικές οδούς ως και σε εκκατα-
λειμένα τμήματα τους και σε ειδηροδρομικές γραμμές)
Εμβαδόν = 4000τμ – Πρόσωπο = 45.00μ – Βάθος = 50.00μ

Αρτιότητα κατά παρέκκλιση • (χωρίς πρόσωπο σε δρόμο)
Εμβαδόν = 4.000 τμ (ηρο 31.12.2003)
• (για πρόσωπα σε Διεθνείς, Εθνικές, Επαρχιακές, Δημοτικές και Κοινοτικές οδούς ως και σε εκκατα-
λειμένα τμήματα τους και σε ειδηροδρομικές γραμμές)
Εμβαδόν = 2.000 τμ – Πρόσωπο = 25,00μ – Βάθος = 40,00μ (ηρο 17.10.1978)
Εμβαδόν = 1200 τμ – Πρόσωπο = 20,00μ – Βάθος = 35,00μ (ηρο 12.09.1964)
Εμβαδόν = 750 τμ – Πρόσωπο = 10,00μ – Βάθος = 15,00μ (ηρο 12.11.1962)
• (εντός της ζώνης πόλεων κ οικισμών & ηρο 24.04.1977)
Εμβαδόν = 2.000 τμ

ΔΗΛΩΣΗ ΜΗΧΑΝΙΚΟΥ Ν.651/77

Η κάτωθι υπογεγραμμένη Βρούτση Βασιλική, Πολιτικός Μηχανικός, δηλώνω σύμφωνα με το νόμο, ότι το γήπεδο με στοιχεία Ε '1,2,3,,,25,26,1' επιφάνειας 1.324,77 τ.μ., επ' ονόματι 'ΜΑΓΚΟΥ', το οποίο βρίσκεται στη θέση 'ΑΓΙΟΣ ΔΗΜΗΤΡΙΟΣ',εντός κτηματικής περιφέρειας τοπικής κοινότητας Γαλανάδου, δημοτικής ενότητας Νάξου, δήμου Νάξου και μικρών Κυκλάδων, νήσου Νάξου, και φαίνεται στο παρόν τοπογραφικό διάγραμμα, ιδιοκτησίας:

κληρονόμων ΚΕΡΡΑ ΔΗΜΗΤΡΙΟΥ

- α. Είναι ΕΚΤΟΣ ΟΙΚΙΣΜΟΥ, ΕΚΤΟΣ ΖΩΕ , ΕΚΤΟΣ NATURA 2000 και εντός ζώνης οικισμού
- β. Είναι μη άρτιο και μη οικοδομήσιμο
- γ. Δεν εμπήντει στις διατάξεις του Ν.1337/83 και δεν έχει υποχρέωση εισφοράς σε γη και σε χρήμα

Η ΜΗΧΑΝΙΚΟΣ

ΔΗΛΩΣΗ ΙΔΙΟΚΤΗΤΗ (Ν.4030/11)

Ο Δημητρίος Κερρά, ιδιοκτήτης του γηπέδου επ' ονόματι 'ΜΑΓΚΟΥ' στη θέση 'ΑΓΙΟΣ ΔΗΜΗΤΡΙΟΣ', δηλώνω ότι:

- τα αρχικά και υλοποιημένα όρια του γηπέδου με στοιχεία '1,2,,,25,26,1' επιφάνειας 1.324,77 τ.μ., το οποίο βρίσκεται εντός κτηματικής περιφέρειας τοπικής κοινότητας Γαλανάδου, δημοτικής ενότητας Νάξου, δήμου Νάξου και μικρών Κυκλάδων, νήσου Νάξου, υπεδείχθησαν από εμένα και
- ευθύνομαι για την ακρίβεια των δηλούμενων ορίων του γηπέδου και η αποτύπωση του έγινε μετά από εντολή μου.

Ο ΔΗΛΩΩ

ΣΤΟΙΧΕΙΑ ΗΛΕΚΤΡΟΝΙΚΗΣ ΥΠΟΒΟΛΗΣ(Αρθρο 3, παρ.4 Υ.Α. 27623/1752/ΦΕΚ2216Β'/14-6-2018)

Το παρόν διάγραμμα υποβλήθηκε ηλεκτρονικά στον ψηφιακό υποδοχέα του ΝΠΔΔ 'Ελληνικό Κτηματολόγιο' και έλαβε μοναδικό Κωδικό Ηλεκτρονικού Διαγράμματος (ΚΗΔ) -----

ΕΜΒΑΔΟΝ ΓΗΠΕΔΟΥ: Ε (1,2,3,,,25,26,1) = 1.324,77 τ.μ.

ΠΑΡΑΤΗΡΗΣΕΙΣ:

- α. Απόσταση από θάλασσα 4,2 km και απόσταση από όριο πλησιέστερου οικισμού (Γαλανάδο) 230 m
- β. Οι διαστάσεις και το εμβαδόν υπολογίστηκαν αναλυτικά από τις συντεταγμένες κορυφών.
- γ. Οι συντεταγμένες των κορυφών του οικοπέδου που αναφέρονται στο Τοπογραφικό Διάγραμμα είναι στο Ελληνικό Γεωδαιτικό Σύστημα Αναφοράς 1987 (Ε.Γ.Σ.Α. '87)
- δ. Η εξάρτηση από το Ε.Γ.Σ.Α. '87 πραγματοποιήθηκε με παρατηρήσεις που διεξήχθησαν κάνοντας χρήση του σταθμού RTCM-REF 0039 του ιδιωτικού δικτύου SmartNet της εταιρίας Metrica ΑΕ με συντεταγμένες (Χ,Υ)=(622586.928,4106369.289)
- ε. Για τις μετρήσεις χρησιμοποιήθηκε GNSS δέκτης Leica GS08 GNSS με Serial Number 1851269 με καταγραφή ευκνοτήτων L1 και L2 του συστήματος GPS και GLONASS.
- ετ. Τίτλος ιδιοκτησίας: Πώληση ακινήτου με αριθμό 1846/11-09-1987 της ευμβολαιογράφου Νάξου Μαρίας Πραίνου
- ς. Δεν έχει γίνει έλεγχος τίτλων ιδιοκτησίας
- η. Εντός του γηπέδου υπάρχει ισόγειο κτίσμα (περιεστηρίνας) Ε=8,56 τ.μ. και ισόγεια αποθήκη Ε= 17,55 τ.μ.
- θ. Στο γήπεδο υπάρχει εημείο υδροπηγής (πηγάδι) με αριθμό ΕΜΣΥ----- η χρήση του οποίου, σύμφωνα με τον τίτλο κτήσης, ανήκει κατά το ήμισυ στο γήπεδο

ΕΡΓΟΔΟΤΗΣ	Δ η μ η τ ρ ι ο ς Κ ε ρ ρ ά ς	
ΕΡΓΟ	ΑΠΟΤΥΠΩΣΗ ΙΔΙΟΚΤΗΣΙΑΣ	
ΘΕΣΗ	Άγιος Δημήτριος τ.κ. Γαλανάδου Νάξου ΔΗΜΟΥ ΝΑΞΟΥ & ΜΙΚΡΩΝ ΚΥΚΛΑΔΩΝ	
ΜΕΛΕΤΗΤΗΣ :	ΒΕΝΙΕΡΗΣ ΕΜΜΑΝΟΥΗΛ ΑΡΧΙΤΕΚΤΩΝ ΜΗΧΑΝΙΚΟΣ	
		ΙΑΝΟΥΑΡΙΟΣ 2018
Σ Χ Ε Δ Ι Ο ΤΟΠΟΓΡΑΦΙΚΟ ΔΙΑΓΡΑΜΜΑ ΤΟΠΟΓΡΑΦΙΚΟ ΔΙΑΓΡΑΜΜΑ ΓΗΠΕΔΟΥ 1,2,...,26,1 ΕΜΒΑΔΟΥ 1.324,77 Τ.Μ.		ΑΡ. ΣΧΕΔΙΟΥ Τ1 ΚΛΙΜΑΚΑ 1/250
ΥΠΟΓΡΑΦΗ	ΣΦΡΑΓΙΔΑ	