
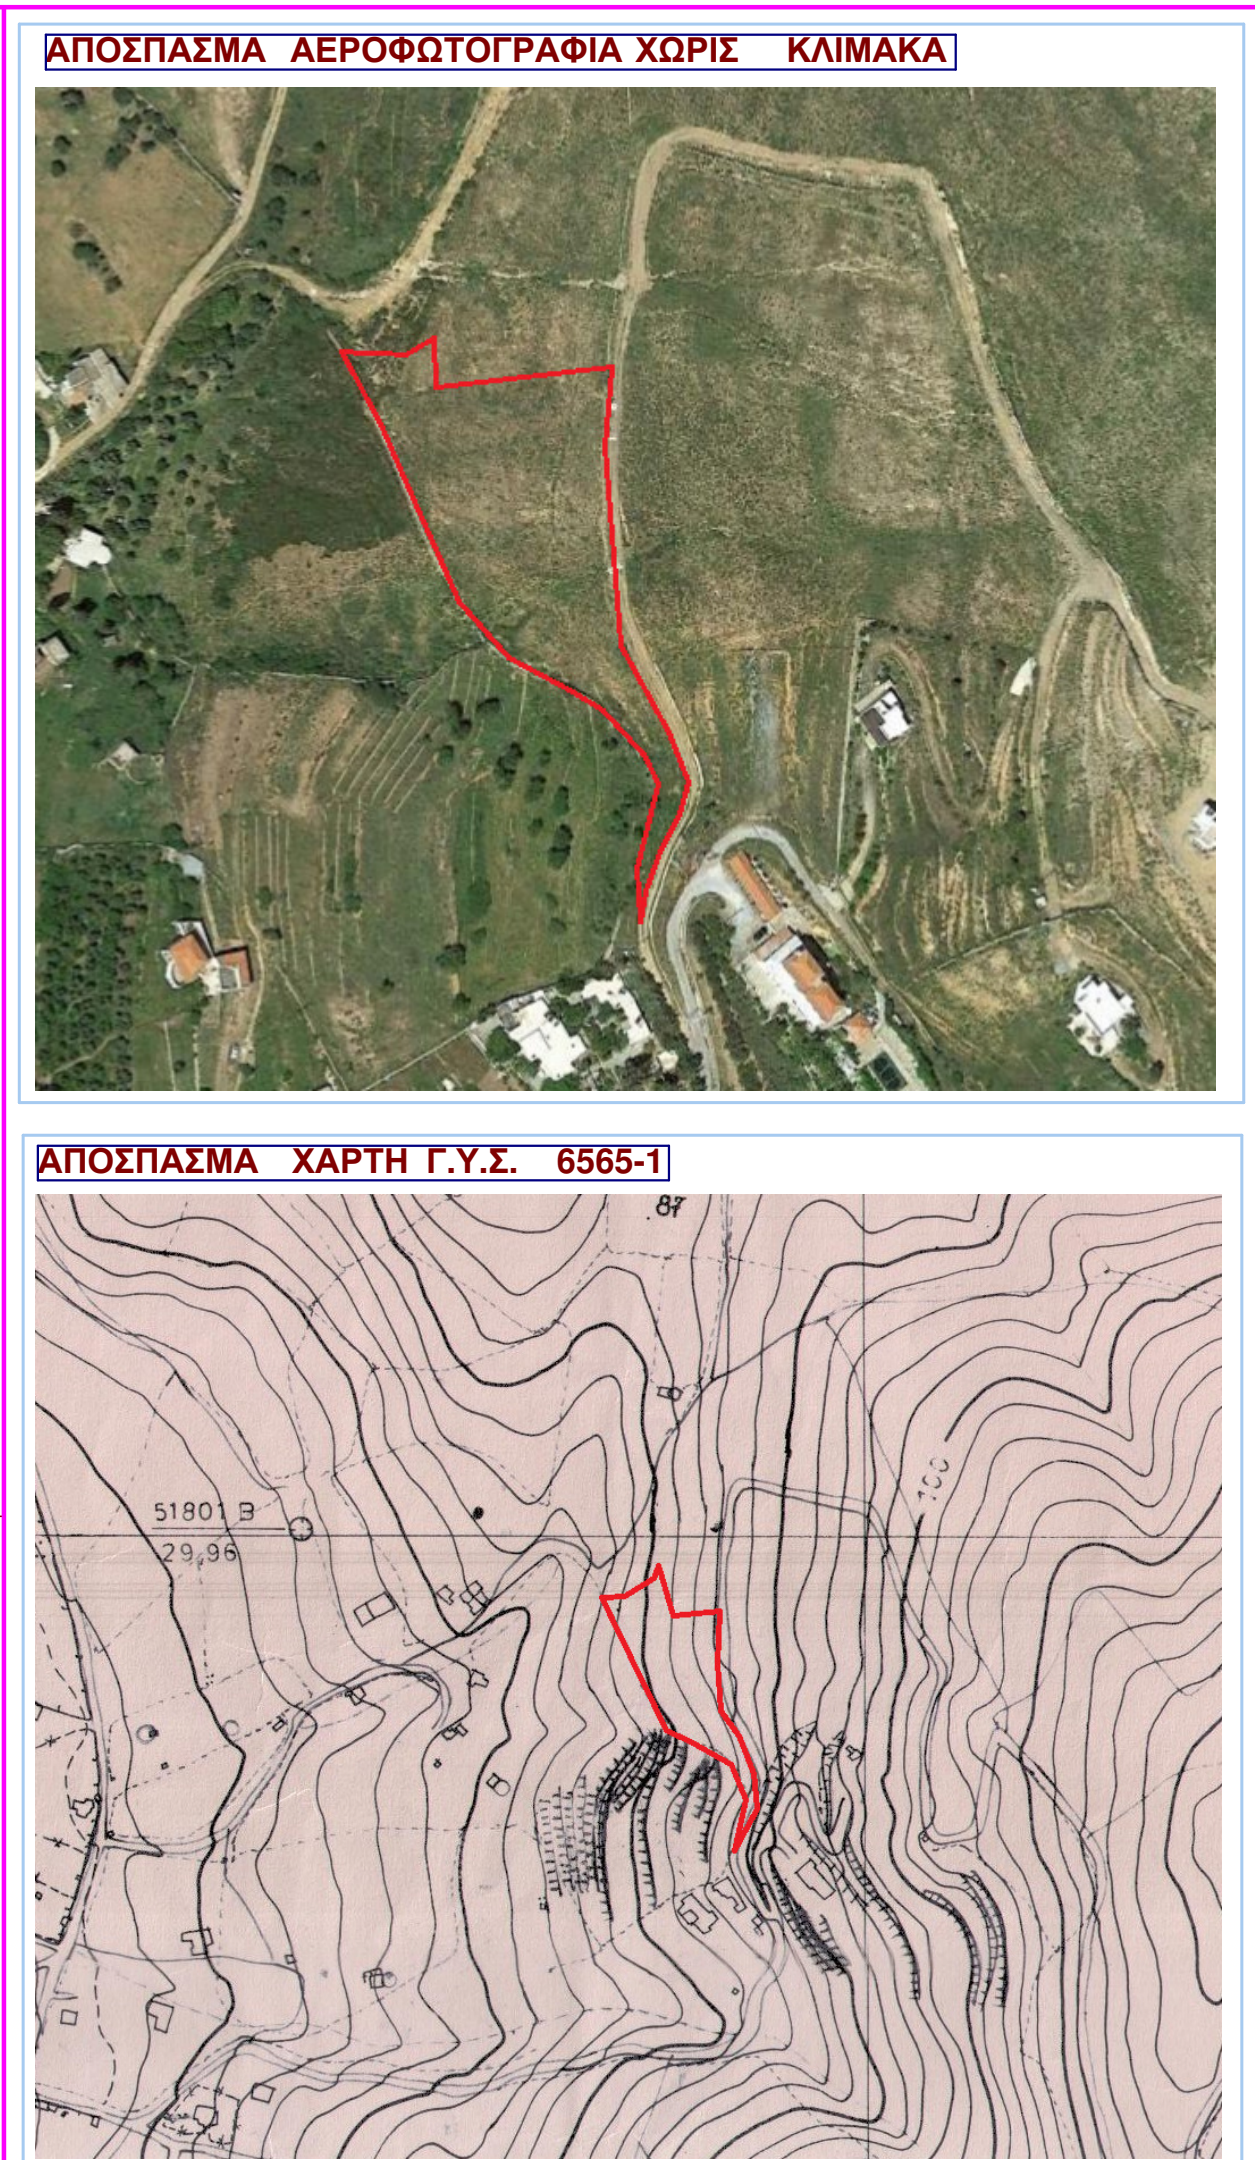


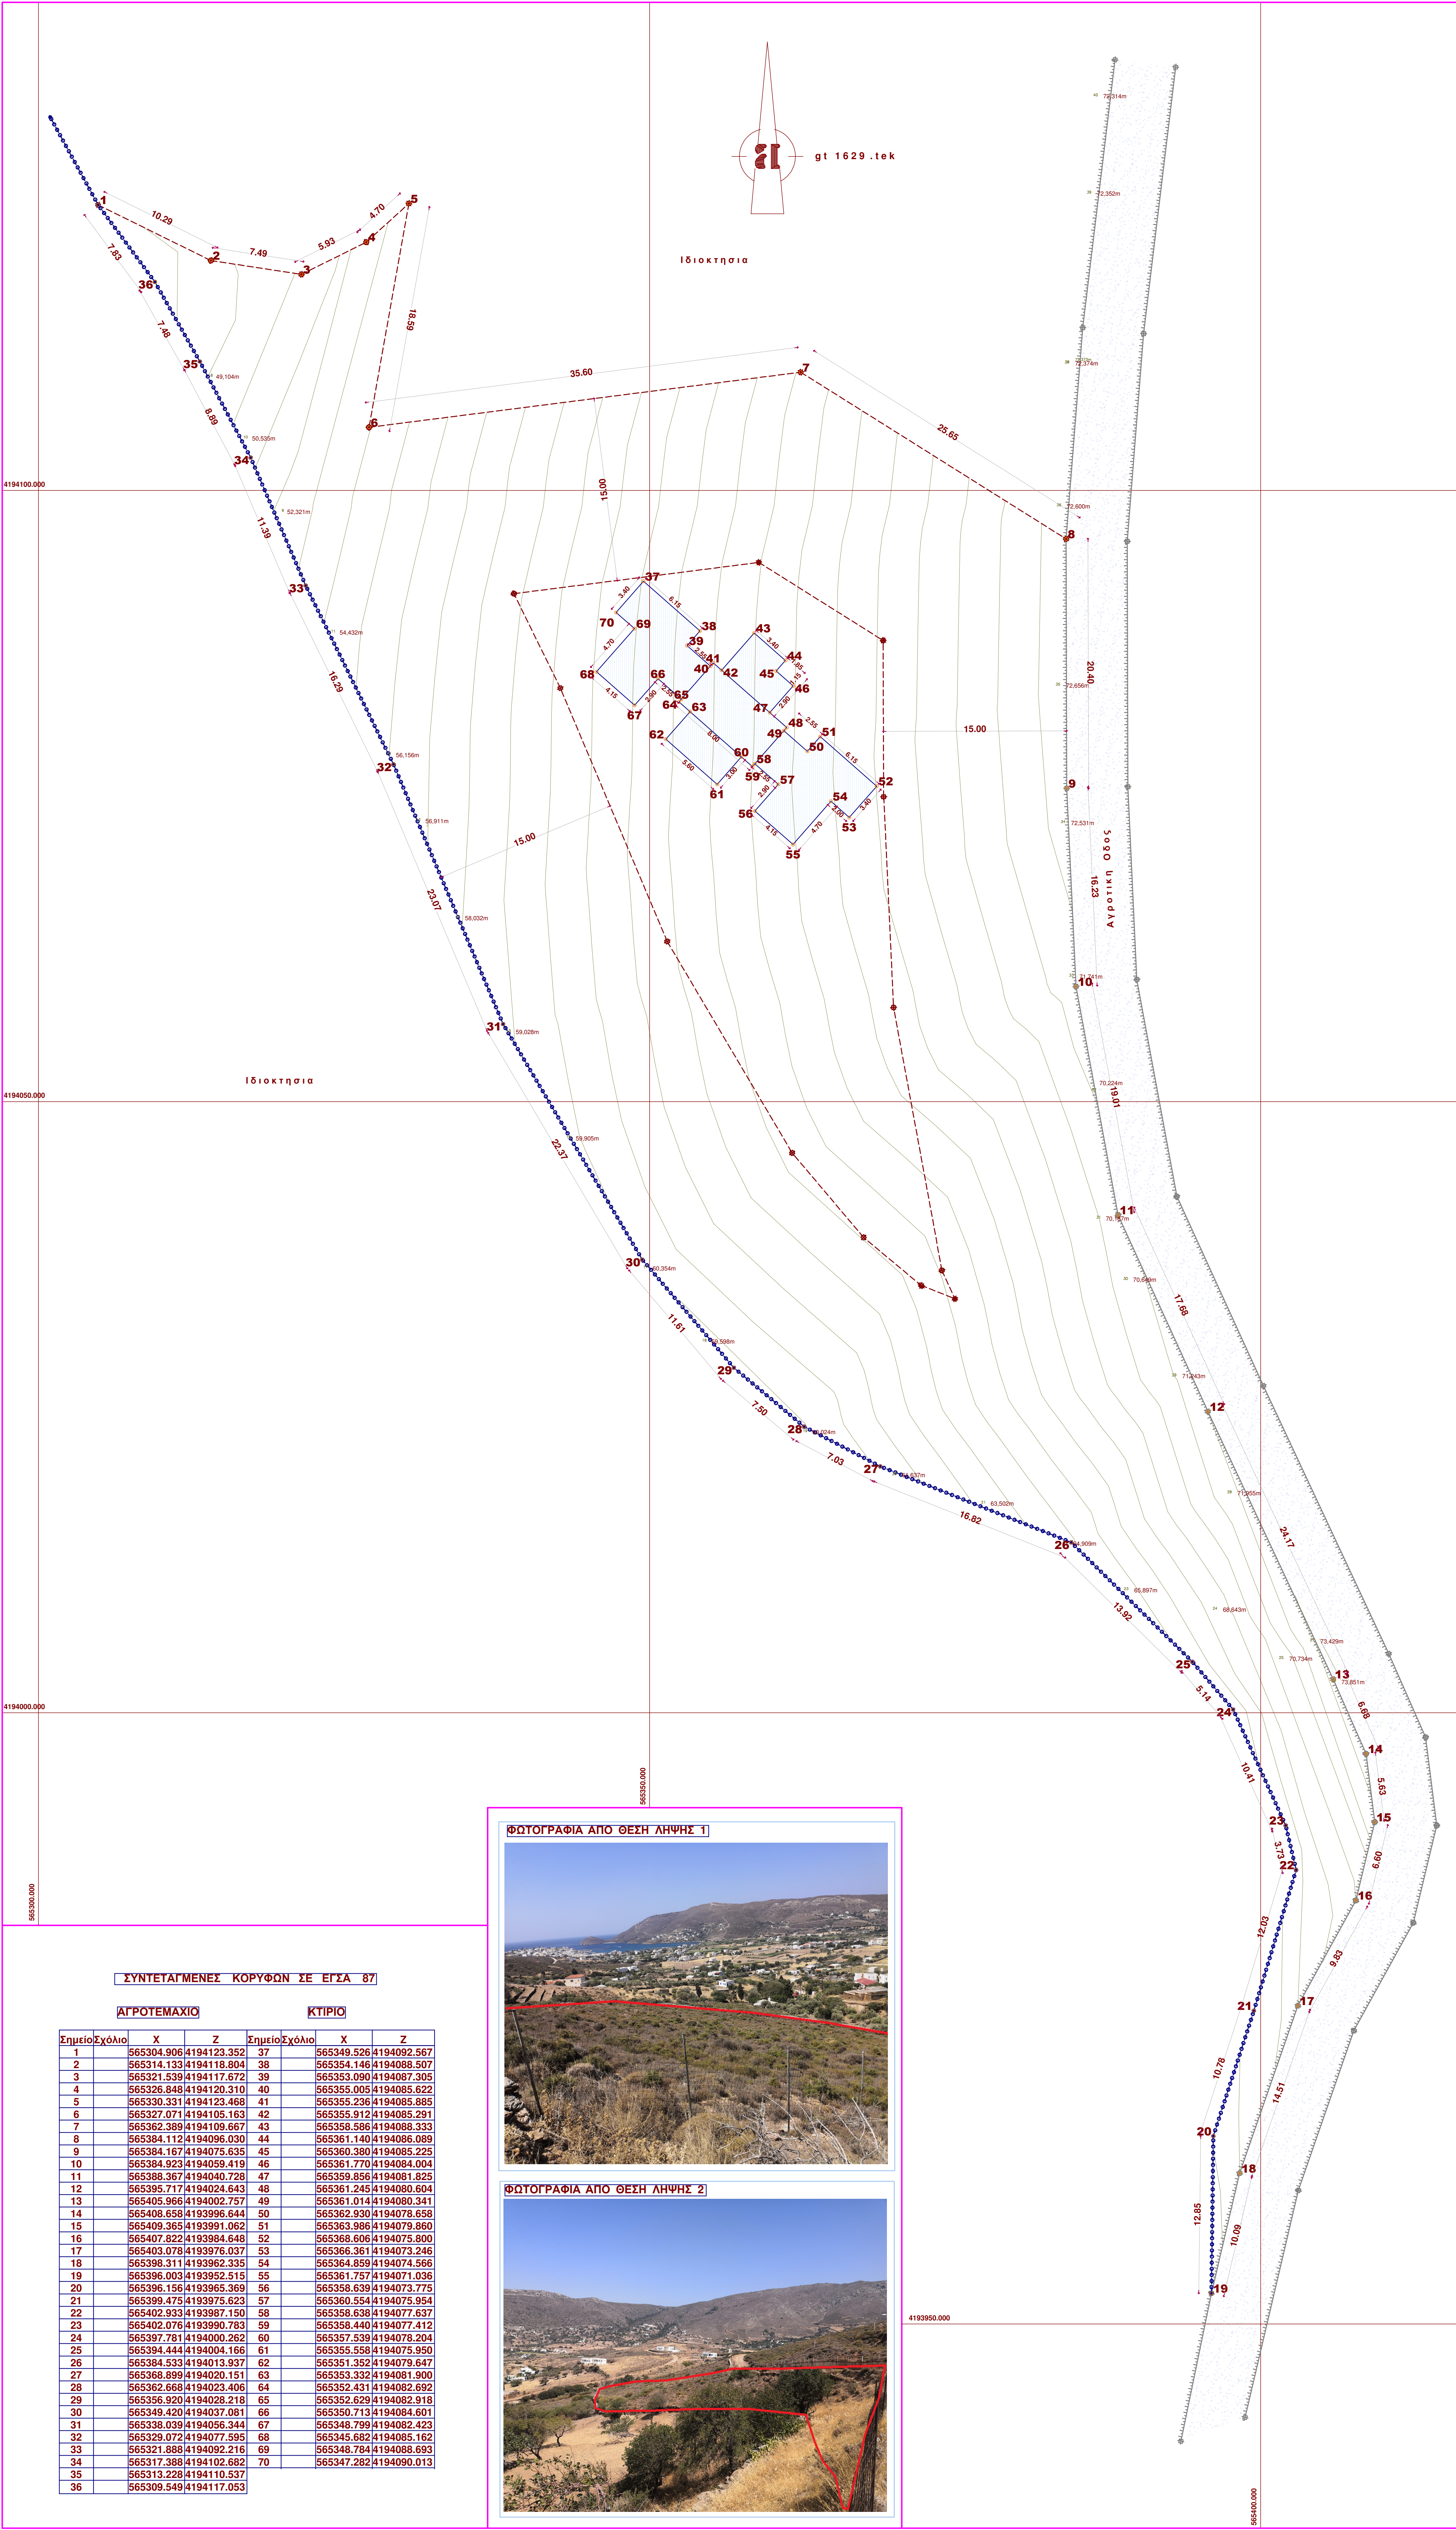

ΥΠΟΜΝΗΜΑ ΣΥΒΟΛΙΣΜΟΥ	
	οριο ιδιοκτησίας
	Παχος εξωτερικού τοιχου da 0,40 - 0,60 m.
	Οριο από συμπνομή
	Φύση (πρασιν - φρυδι - παραβολή)
	κυρία ισοψηφής
	δευτερευουσα ισοψηφής
	Θεση ληψης φωτογραφίας
	Στυλος Δ.Ε.Η.
	Στυλος Ο.Τ.Ε.

Δήλωση Ν. 651 / 77

Το αγροτεμαχιο (1-2-3-4.....35-36-1) είναι εκτός σχεδίου δεν αποκοπτεται από μεγαλύτερη έκταση και σύμφωνα με την ισχύουσα πολεοδομική νομοθεσία είναι αρτο και οικοδομήσιμο .

ο μηχανικός

ΓΡΗΓΟΡΗΣ ΔΗΜ. ΣΟΥΛΙΑΣ

ΠΡΟΤΥΠΙΚΟΣ ΔΙΑΜΕΤΡΗΤΗΣ

ΜΕΛΟΣ 2011

ΕΠΙΣΤΗΜΟΝΙΚΟ ΣΥΜΒΟΥΛΙΟ

ΑΔΩΝ 543201175 - ΔΩΝ ΑΝΔΡΟΥ

ΔΗΛΩΣΗ ΙΔΙΟΚΤΗΤΗ (Ν. 4030/2011)

Η κατωθι υπογεγραμμενη Νικολετα Ματθαίου δηλώνω ότι :

- Τα ορια αγροτεμαχίου με τα στοιχεία (1-2-3-4.....34-35-36-1) και εμβαδον 5.031,92 τ.μ. που βρίσκεται στη θέση Σαρακηνικο - Γαυριο Δήμου Ανδρού Νήσου Ανδρου υπτεειχθησαν από εμένα και ευθυνομαι για την ακριβεία των δηλουμένων οριων του αγροτεμαχίου.

Ο ΔΗΛΩΝ

Name	Easting	Northing	Elevation
PRS905317915328	577911,944	4184842,098	258,780

Εμβαδον (1-2-3-4.....34-35-36-1) = 5.031,92 m2

ΠΑΡΑΤΗΡΗΣΕΙΣ

α. Το διαγραμμα είναι ενταγμένο στο κρατικό σύστημα συντεταγμένων ΕΣΓΑ 87

β. Οι διαστάσεις και τα εμβαδα υπολογισθηκαν αναλυτικά από τις συνίνες των κορυφών

γ. Η εξάρτηση από το ΕΣΓΑ 87 πραγματοποιήθηκε με το σύστημα GPS και κανοντας χρήση του Ελληνικού Συστήματος Εντοπισμού - ΝΕΡΟΣ

δ. Η απόσταση του αγροτεμαχίου από την θάλασσα είναι τετρακόσια ογδοντα πέντε μέτρα 1.076,00 μ.

Επίσης δεν εμπίπτει στο Νομό 1337 / 1983 .

Οροι δομησεως

Οροι δομησεως (Εκτος Σχεδίου)

π.δ. 04/11/2011 Φ.Ε.Κ. 291 Δ !

Ε = 4000,00 τ.μ. (κατο κανονο)

Προσωση σε δρομο 25,00μ.

Αποστασεις : Απ (απο οριο αγροτ.) >= 15,00 μ.

Απ (απο οδο) >= 15,00 μ.

Καλυψη = MEK = 200*(Εοικ-4000)Χ0,01 = max 400,00 τμ

Δομηση = MEΔ = 150*(Εοικ-4000)Χ0,01 = max 400,00 τμ

Αριθμος οροφων = 2 ,Υψος κτιριου α) μονοροφο <= + 4,00 μ.

β) διωροφο <= + 7,50 μ.

ΕΠΙΧΕΙΡΗΣΗ:	ΝΙΚΟΛΕΤΑ ΜΑΤΘΑΙΟΥ		
ΕΠΩ:	ΤΡΕΙΣ ΝΕΕΣ ΙΣΟΓΕΙΕΣ ΚΑΤΟΙΚΙΕΣ ΜΕ ΥΠΟΓΕΙΟ		
ΒΕΣΗ:	ΕΠΙΣΤΗΜΟΝΙΚΟ ΣΥΜΒΟΥΛΙΟ ΔΗΜΟΤΙΚΗΣ ΕΠΙΧΕΙΡΗΣΗΣ ΔΗΜΟΥ ΑΝΔΡΟΥ ΝΗΣΟΥ ΑΝΔΡΟΥ Π.Ε. ΑΝΔΡΟΥ ΠΕΡΙΦΕΡΕΙΑ ΝΟΤΙΟΥ ΑΙΓΑΙΟΥ		
ΜΕΛΕΤΗ:	ΤΟΠΟΓΡΑΦΙΚΗ		
ΒΕΛΑ ΕΣΧΕΔΙΟΥ:	ΤΟΠΟΓΡΑΦΙΚΟ ΔΙΑΓΡΑΜΜΑ		
ΚΛΙΜΑΚΑ:	1 : 200	ΟΚΤΩΒΡΙΟΣ 2020	T 1
ΑΝΑΔΕΙΧΝΟΜΕΝΟΣ:	Α		
ΜΕΛΕΤΗΤΕΣ:	ΑΡΧΙΤΕΚΤΟΝΕΣ ΜΙΚ. ΠΟΛΙΤΙΚΟΙ ΜΙΚ. ΜΕΤΕΩΡΟΛΟΓΟΙ ΜΙΚΑΔΑ ΜΙΚ.		
ΕΠΙΣΤΗΜΟΝΙΚΟ ΣΥΜΒΟΥΛΙΟ:	ΓΡΗΓΟΡΗΣ ΔΗΜ. ΣΟΥΛΙΑΣ		



ΣΥΝΤΕΤΑΓΜΕΝΕΣ ΚΟΡΥΦΩΝ ΣΕ ΕΓΣΑ 87					
ΑΓΡΟΤΕΜΑΧΙΟ			ΚΤΙΡΙΟ		
Σημείο/Σχόλιο	X	Z	Σημείο/Σχόλιο	X	Z
1	565304.906	4194123.352	37	565349.526	4194092.567
2	565314.133	4194118.804	38	565354.146	4194088.507
3	565321.539	4194117.672	39	565353.090	4194087.305
4	565326.848	4194120.310	40	565355.005	4194085.622
5	565330.331	4194123.468	41	565355.236	4194085.885
6	565327.071	4194105.163	42	565355.912	4194085.291
7	565362.389	4194109.667	43	565358.586	4194088.333
8	565384.112	4194096.030	44	565361.140	4194086.089
9	565384.167	4194075.635	45	565360.380	4194085.225
10	565384.923	4194059.419	46	565361.770	4194084.004
11	565388.367	4194040.728	47	565359.856	4194081.825
12	565395.717	4194024.643	48	565361.245	4194080.604
13	565405.966	4194002.737	49	565361.014	4194080.341
14	565408.658	4193996.644	50	565362.930	4194078.658
15	565409.365	4193991.062	51	565363.986	4194079.860
16	565407.822	4193984.648	52	565368.606	4194075.800
17	565403.078	4193976.037	53	565366.361	4194073.246
18	565398.311	4193962.335	54	565364.899	4194074.566
19	565396.003	4193952.515	55	565361.757	4194071.036
20	565396.156	4193965.369	56	565358.639	4194073.775
21	565399.475	4193975.623	57	565360.554	4194075.954
22	565402.933	4193987.150	58	565358.638	4194077.637
23	565402.076	4193990.783	59	565358.440	4194077.412
24	565397.781	4194000.262	60	565357.539	4194078.204
25	565394.444	4194004.166	61	565355.558	4194075.950
26	565384.533	4194013.937	62	565351.352	4194079.647
27	565386.899	4194020.151	63	565345.682	4194085.162
28	565362.668	4194023.406	64	565352.431	4194082.692
29	565356.920	4194028.218	65	565352.629	4194082.918
30	565349.420	4194037.081	66	565350.713	4194084.601
31	565338.039	4194056.344	67	565348.799	4194082.423
32	565328.072	4194077.595	68	565345.682	4194085.162
33	565321.888	4194092.216	69	565348.784	4194088.693
34	565317.388	4194102.682	70	565347.282	4194090.013
35	565313.228	4194110.537			
36	565309.549	4194117.053			